
01 · Обмерный план (существующее)

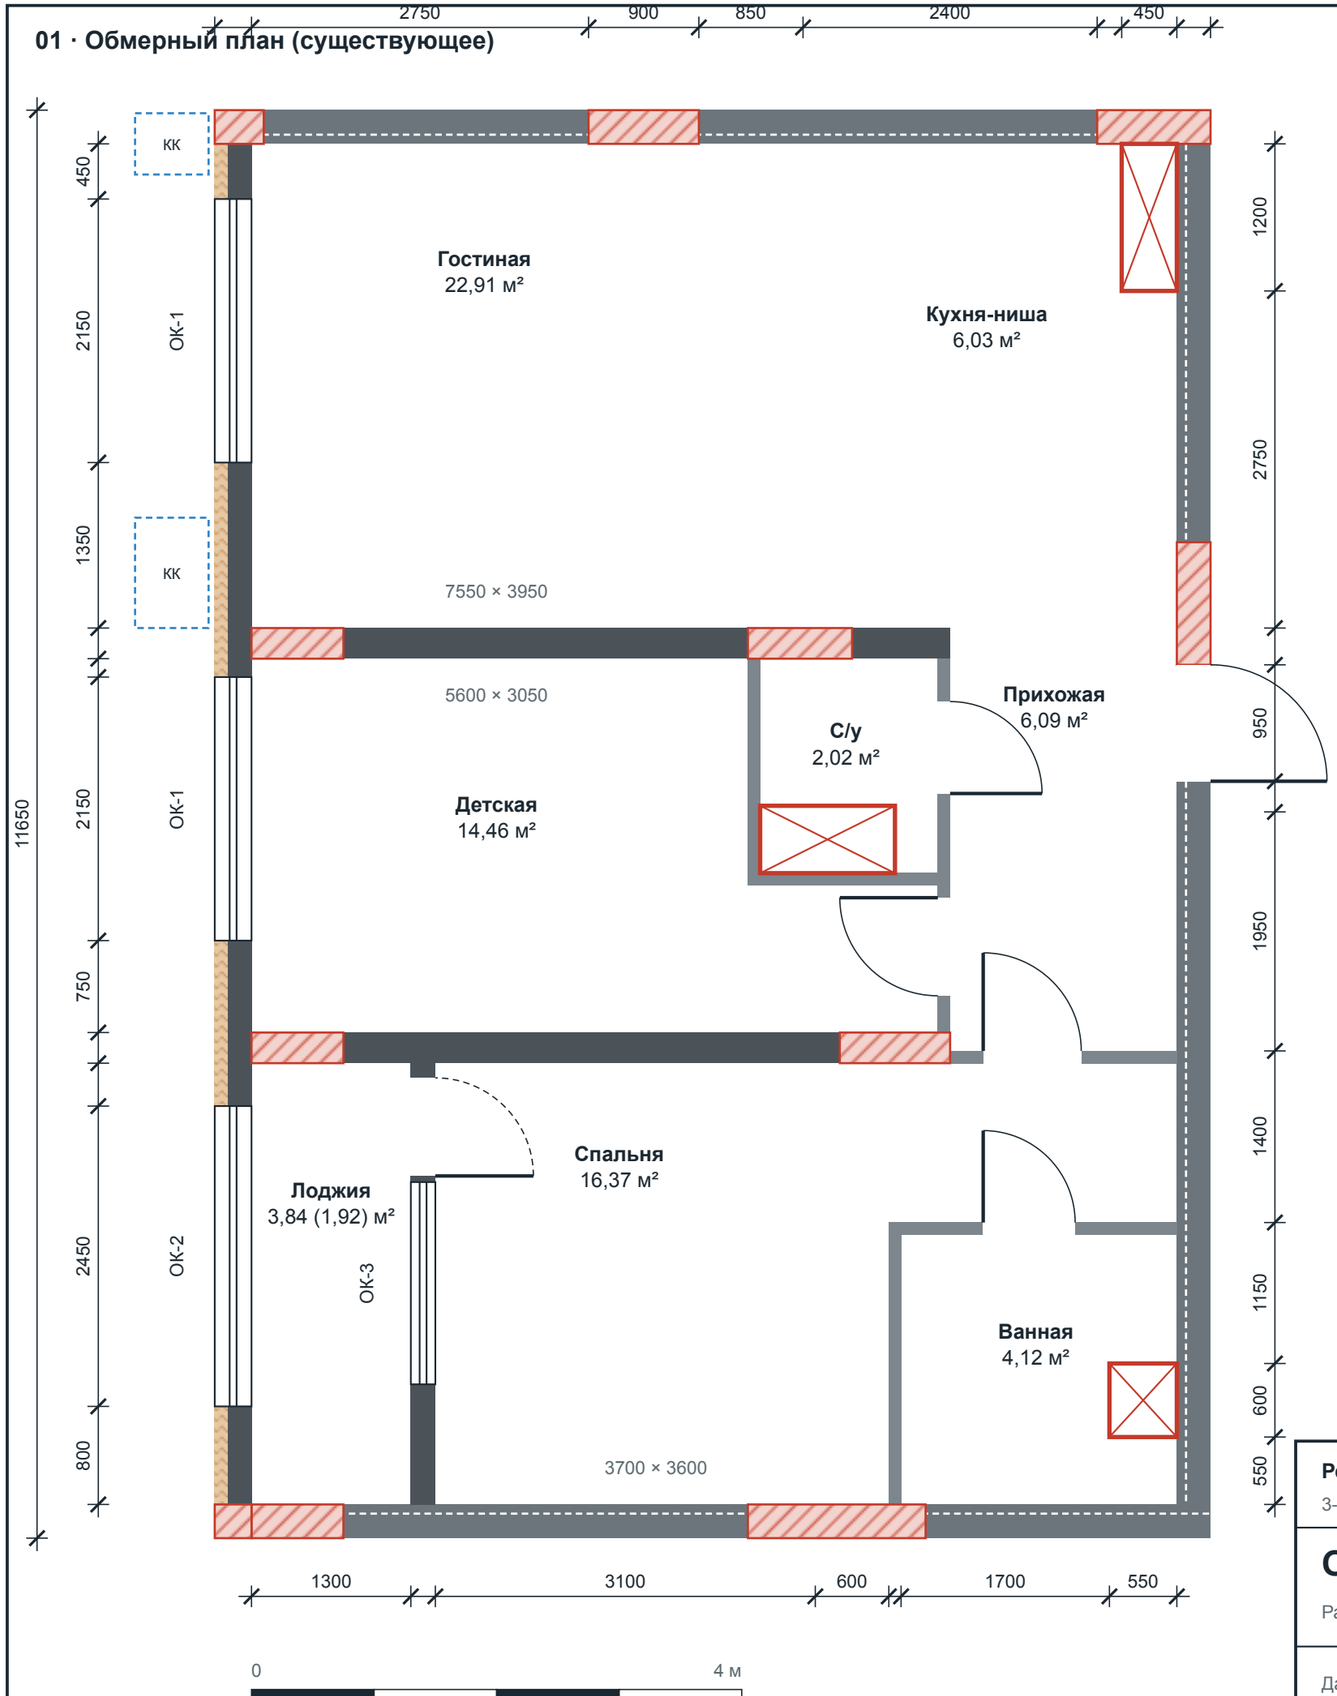

Условные обозначения

- Монолит ж/б, 250 мм — не трогать
- Газоблок 200 мм
- Газоблок 100 мм
- Межквартирная: газоблок + акуст. плита + ГКЛ, 250–275 мм
- Утеплитель фасада
- Сантехнический короб (стояки), люк обязателен
- КК — корзина кондиционера на фасаде

Экспликация помещений

№	Наименование	Площадь, м²
1	Гостиная	22,91
2	Кухня-ниша	6,03
3	Прихожая	6,09
4	Детская	14,46
5	С/у	2,02
6	Спальня родителей	16,37
7	Ванная	4,12
8	Лоджия (к=0,5)	3,84 (1,92)
Итого общая площадь		**73,92**

Проёмы

ОК-1	Окно 2150×2500, низ +0,25 (гостиная, спальня 1)
ОК-2	Остекление лоджии 2450×2500
ОК-3 / БД	Балконный блок: дверь 800 + окно 1650
Д-1	Входная 950×2100
Д-2	Межкомнатная 800×2100
Д-3	Санузловая 750×2100

Ремонт квартиры · ЖК GreenLine Garden-2, блок 2, подъезд 2

3-комн., общая площадь 73,92 м² · концепция «Дала»


Обмерный план (существующее)

Размеры в мм, отметки в м от чистого пола. Высота потолка 3,00 (уточнить)

Стадия: **Эскиз РП**

Дата	Основа	Масштаб	Лист	Листов
13.11.2026	планировка BI Group	1:50	01	10

02 · Демонтаж и монтаж перегородок

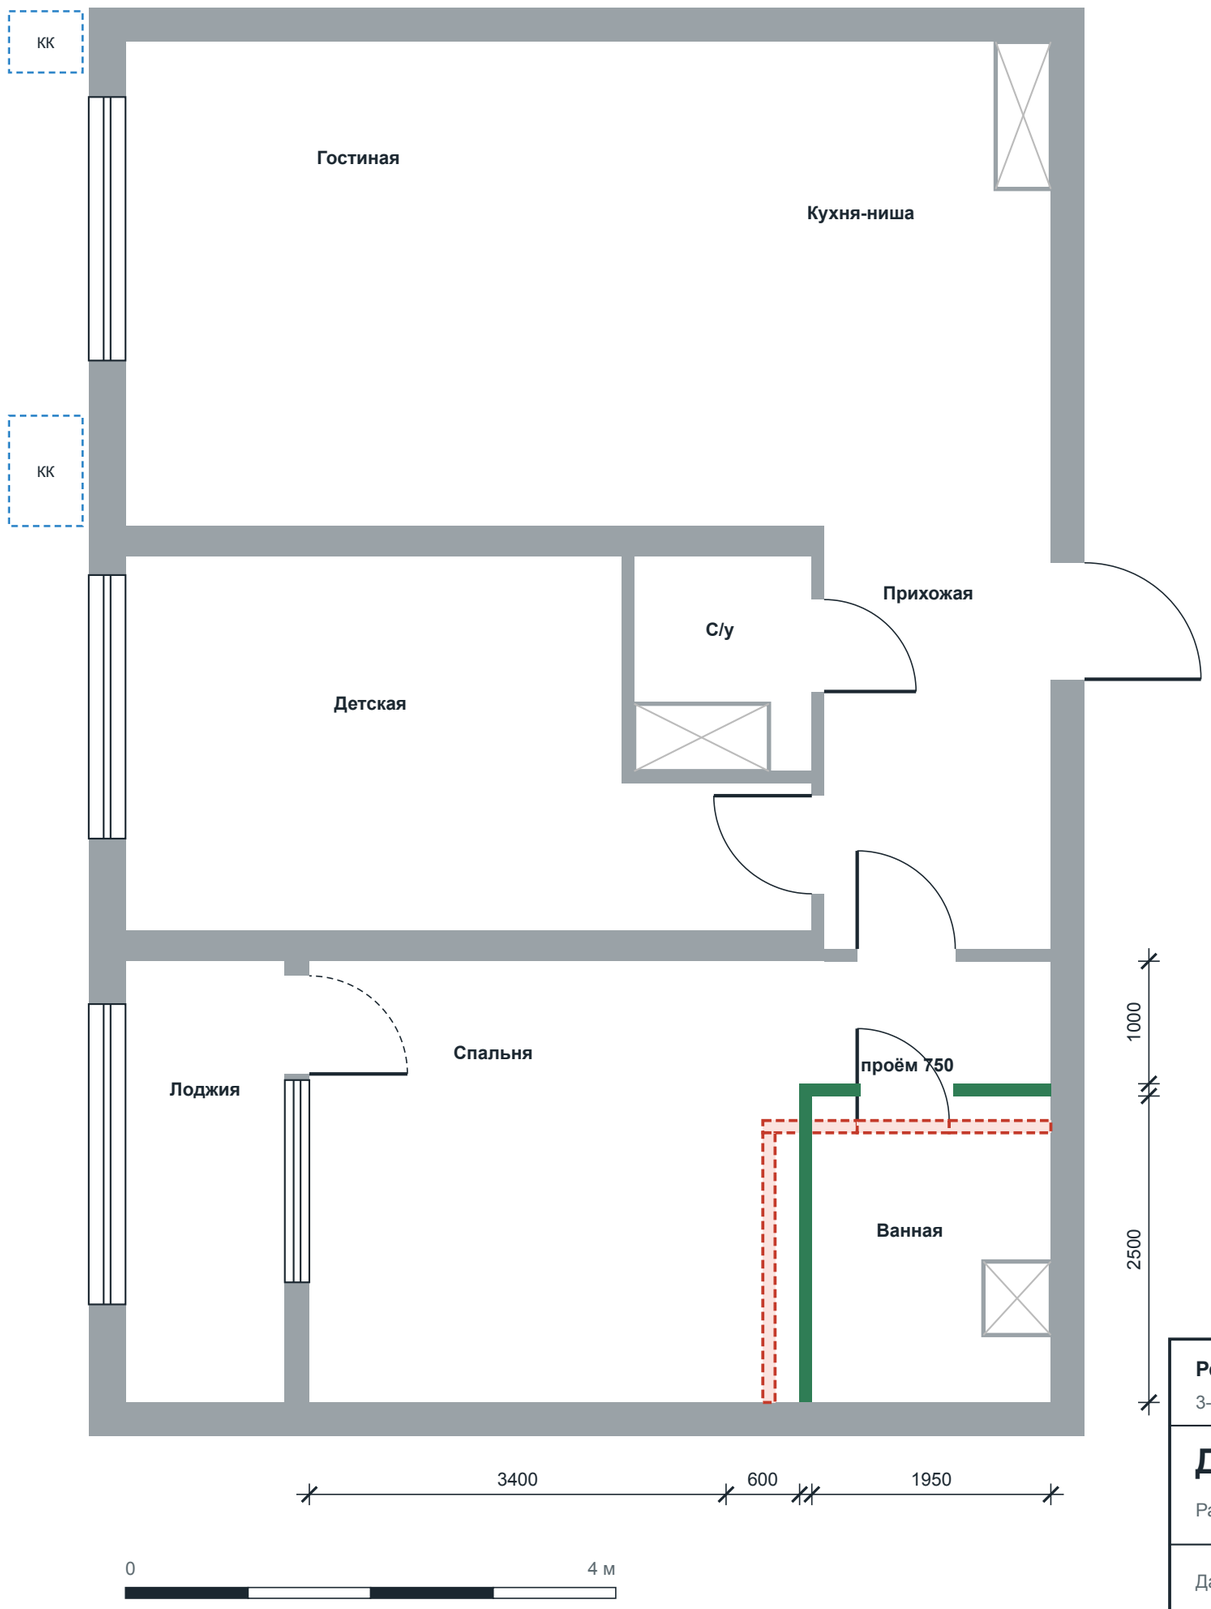

Перенос стены ванной

Демонтаж: газоблок 100 мм, h = 3,0 м	3,8 м.п. / 11,4 м²
Монтаж: газоблок 100 мм D500, армирование через 3 ряда	3,8 м.п. / 9,8 м²
Существующие стены — без изменений	

Что меняется

— Стена между спальней и ванной сдвигается на 300 мм вправо, стена с дверью — на 300 мм к входу в спальню. Ванная становится 1,95×2,50 м (было 2,25×2,20).

— Спальня получает ровную стену 2,6 м под шкаф-купе. Мокрая зона по площади не растёт: 0,6 м² добавляется со стороны входа и 0,66 м² отдаётся спальне.

— Короб со стояками остаётся на месте, внутри ванной. Вентканал не затрагивается.

— Новые стены в ванной — газоблок с обмазочной гидроизоляцией или влагостойкие пазогребневые плиты.

Согласование

— Это перепланировка: меняется конфигурация помещений и техпаспорт. До начала работ — эскизный проект и решение акимата через eGov.

— Полоса 0,6 м² новой ванной оказывается над спальней соседей снизу. Проектировщик должен подтвердить, что это допустимо по СП РК 3.02-101-2012; если нет — стена с дверью остаётся на месте, переносится только боковая.

— Самовольная перепланировка — штраф по ст. 322 КоАП РК и проблемы при продаже и ипотеке.

Ремонт квартиры · ЖК GreenLine Garden-2, блок 2, подъезд 2

3-комн., общая площадь 73,92 м² · концепция «Дала»


Демонтаж и монтаж перегородок

Размеры в мм, отметки в м от чистого пола. Высота потолка 3,00 (уточнить)

Стадия: **Эскиз РП**

Дата	Основа	Масштаб	Лист	Листов
13.11.2026	планировка BI Group	1:50	02	10

03 · План с расстановкой мебели

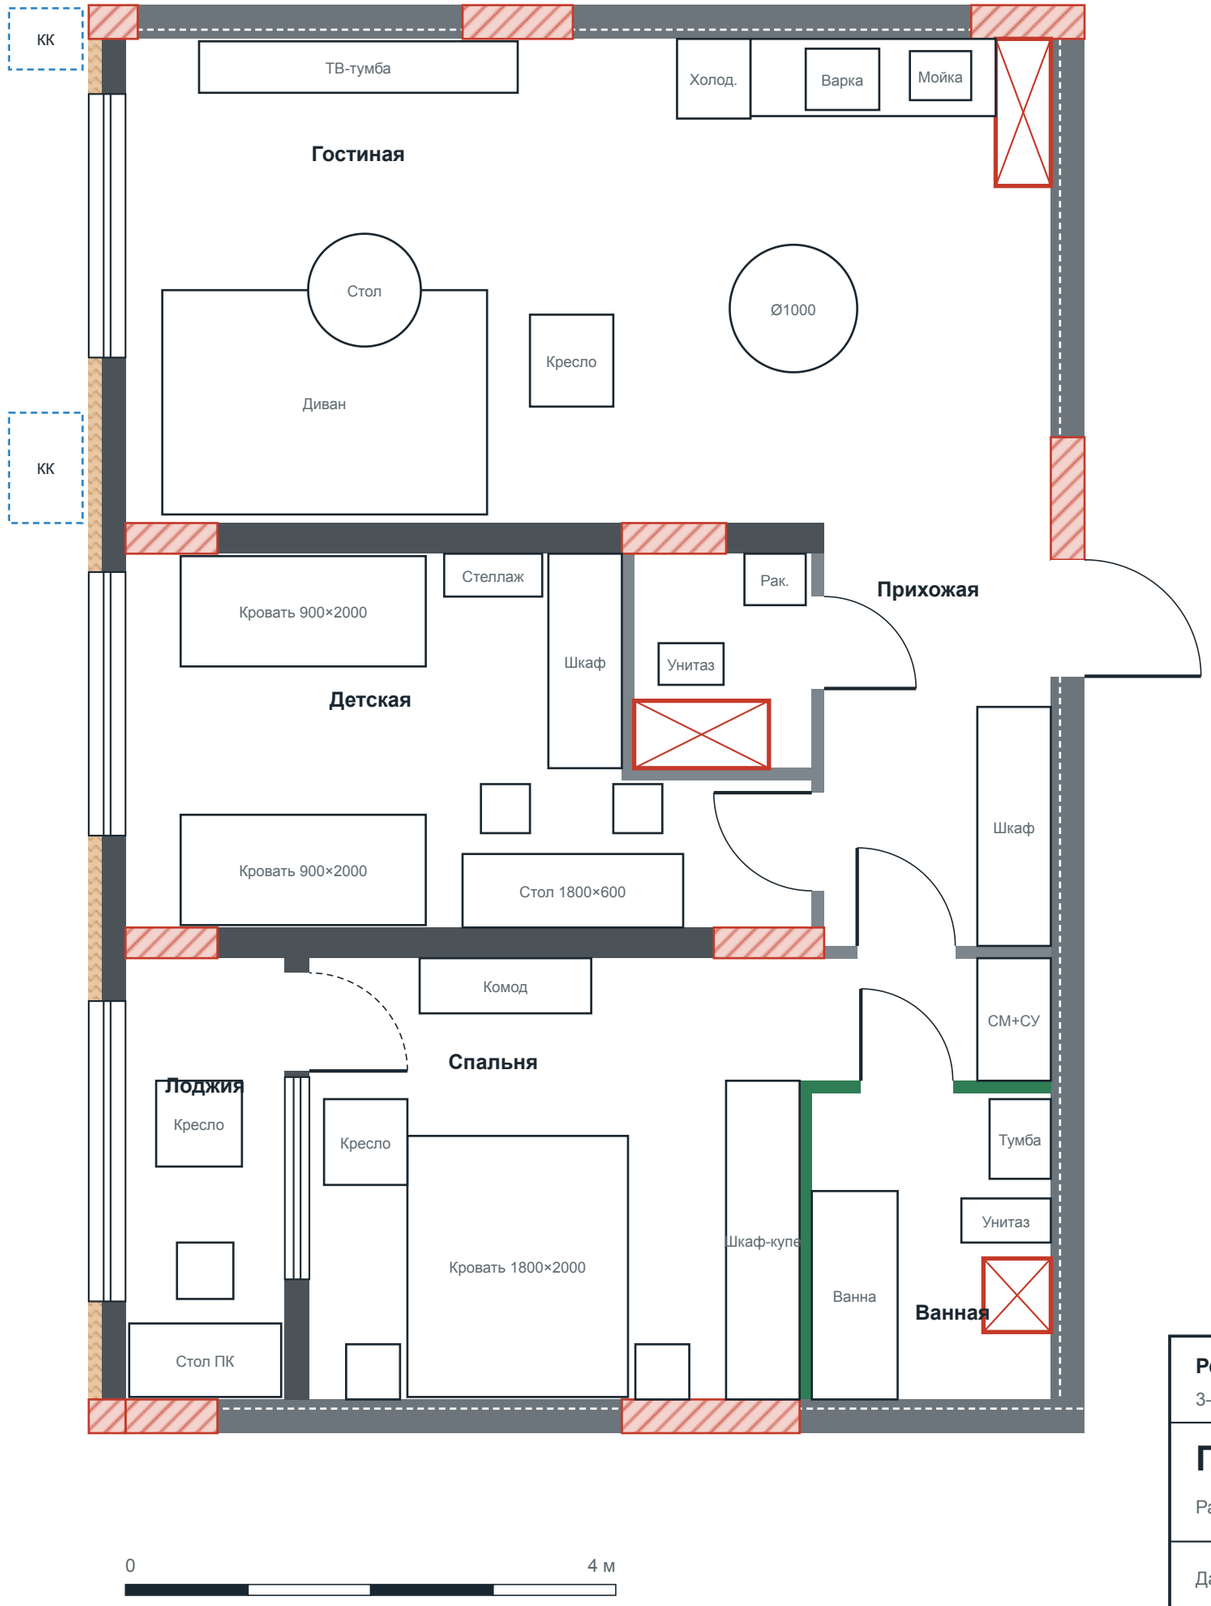

Решения по планировке

— Гостиная: угловой диван к стене детской, ТВ напротив на акцентной стене, кресло у прохода.

— Кухня-ниша 2,6 м линейная: колонна под встроенный холодильник, варочная по центру, мойка у короба со стояками. Стол Ø1000 на 4 места.

— Прихожая: шкаф-купе 600×1950 до потолка.

— Детская: две полноценные кровати 900×2000 вдоль противоположных стен изголовьями от окна, между ними игровая зона 1,2 м. Письменный стол 1800×600 на двоих, шкаф 600 до потолка, стеллаж для игрушек.

— Спальня: стена ванной перенесена (лист 02). Вдоль неё шкаф-купе 2600×600 до потолка. Кровать 1800 изголовьем к наружной стене, напротив — комод с зеркалом, без ТВ (вывод оставлен в резерве).

— У входа в спальню — шкаф-постирочная: стиральная и сушильная машины колонной, за стеной ванной.

— Ванная 1,95×2,50 м: ванна 1700×700 вдоль шкафной стены, подвесной унитаз у стояка, тумба с раковиной 650 у двери.

— Лоджия: рабочее место с компьютером — стол 1240×600 в торце, полка над ним, кресло для отдыха. Нужны утепление, тёплый пол и розетки (листы 04, 06).

Мебель показана габаритами. Проходы не уже 700 мм, перед шкафами — 800 мм.

Ремонт квартиры · ЖК GreenLine Garden-2, блок 2, подъезд 2

3-комн., общая площадь 73,92 м² · концепция «Дала»


План с расстановкой мебели

Размеры в мм, отметки в м от чистого пола. Высота потолка 3,00 (уточнить)

Стадия: **Эскиз РП**

Дата	Основа	Масштаб	Лист	Листов
13.11.2026	планировка BI Group	1:50	03	10

04 · План полов

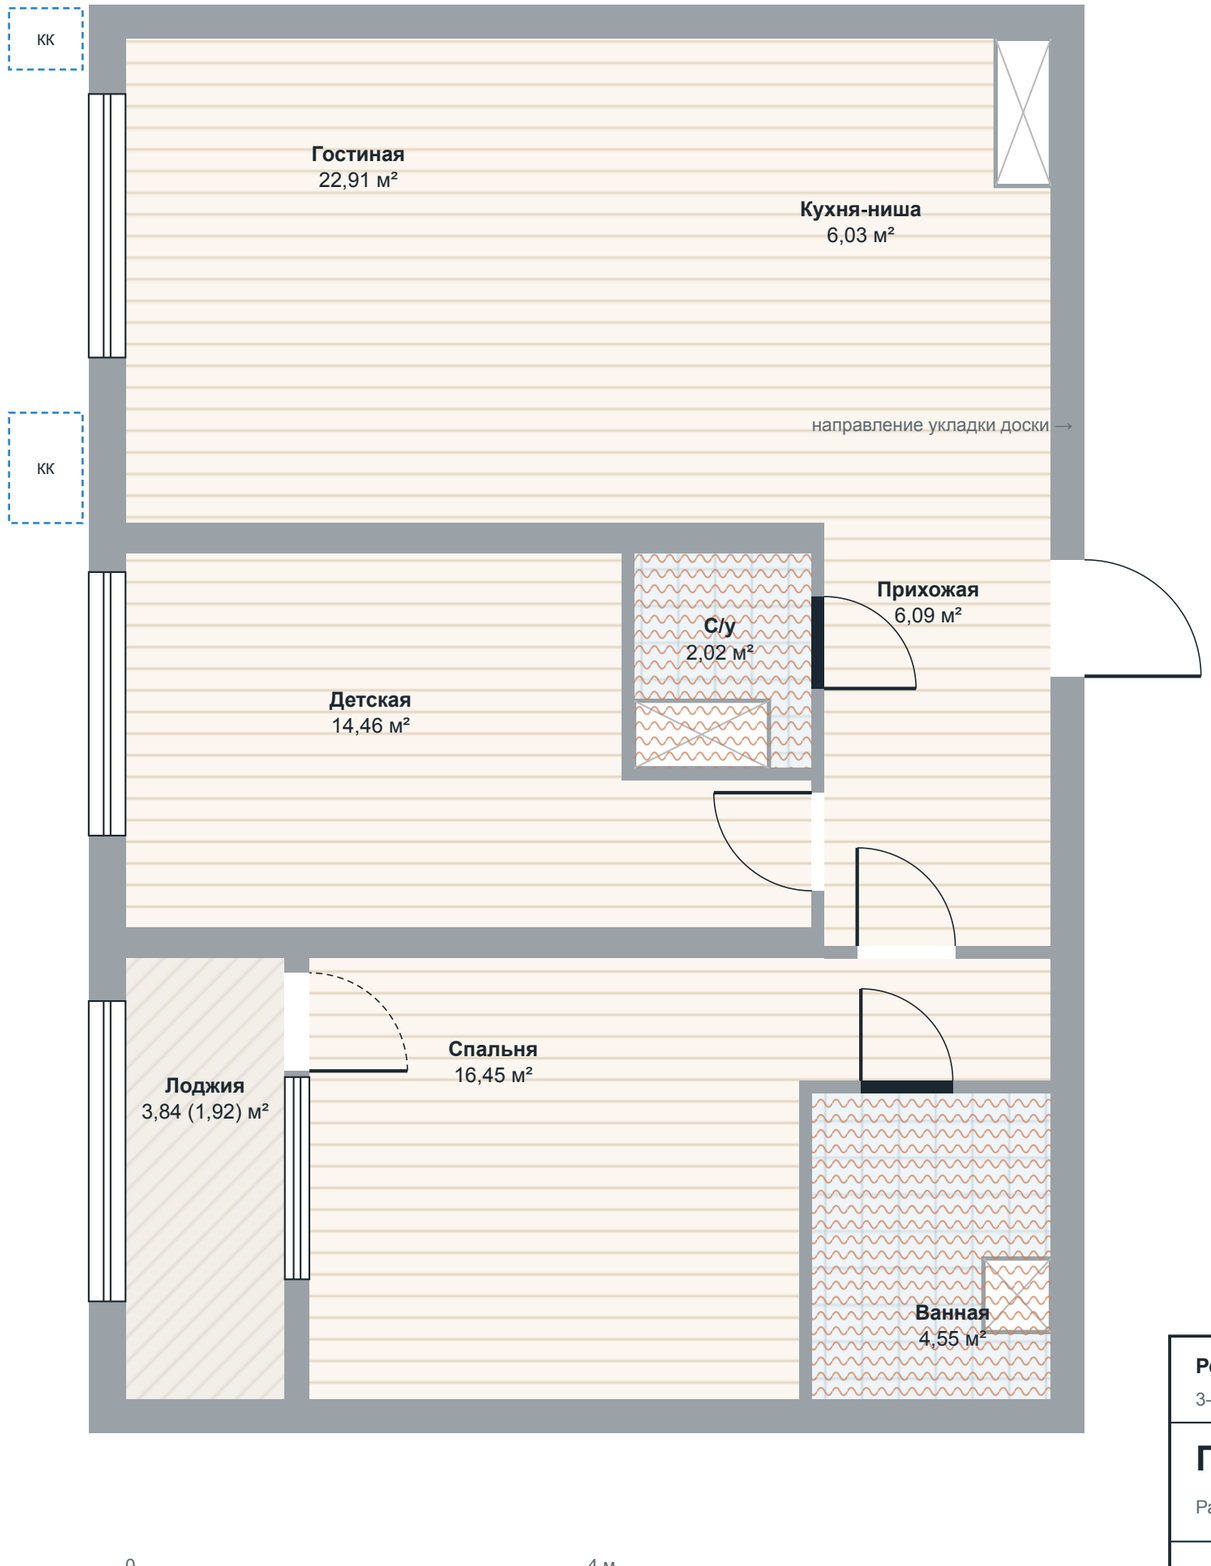

Покрытия пола

Инженерная доска, дуб натур, 180×1200, масло-воск	66,3 м²
Керамогранит 60×60 см, мокрые зоны	6,5 м²
Лоджия: керамогранит под дерево / террасная доска	4,7 м²
Электрический тёплый пол (мат) под плитку	С/у, ванная
Порог-гидробарьер / стык плитка-доска	2 шт.

Пирог пола

— Сухие зоны: стяжка (от застройщика) → грунт → подложка 2 мм → доска/SPC. Отметка чистого пола ±0,000 по всей квартире.

— Мокрые зоны: обмазочная гидроизоляция с заходом на стены 200 мм, в душевой зоне — на 2000 мм, затем мат тёплого пола и плитка на клей.

— Плинтус скрытый или высокий 80 мм в цвет стен — без контрастной полосы по периметру.

— Доска укладывается вдоль длинной оси гостиной (от окна вглубь), без порогов между комнатами.

Ремонт квартиры · ЖК GreenLine Garden-2, блок 2, подъезд 2

3-комн., общая площадь 73,92 м² · концепция «Дала»


План полов

Размеры в мм, отметки в м от чистого пола. Высота потолка 3,00 (уточнить)

Стадия: **Эскиз РП**

Дата	Основа	Масштаб	Лист	Листов
13.11.2026	планировка BI Group	1:50	04	10

05 · Потолки, свет, выключатели

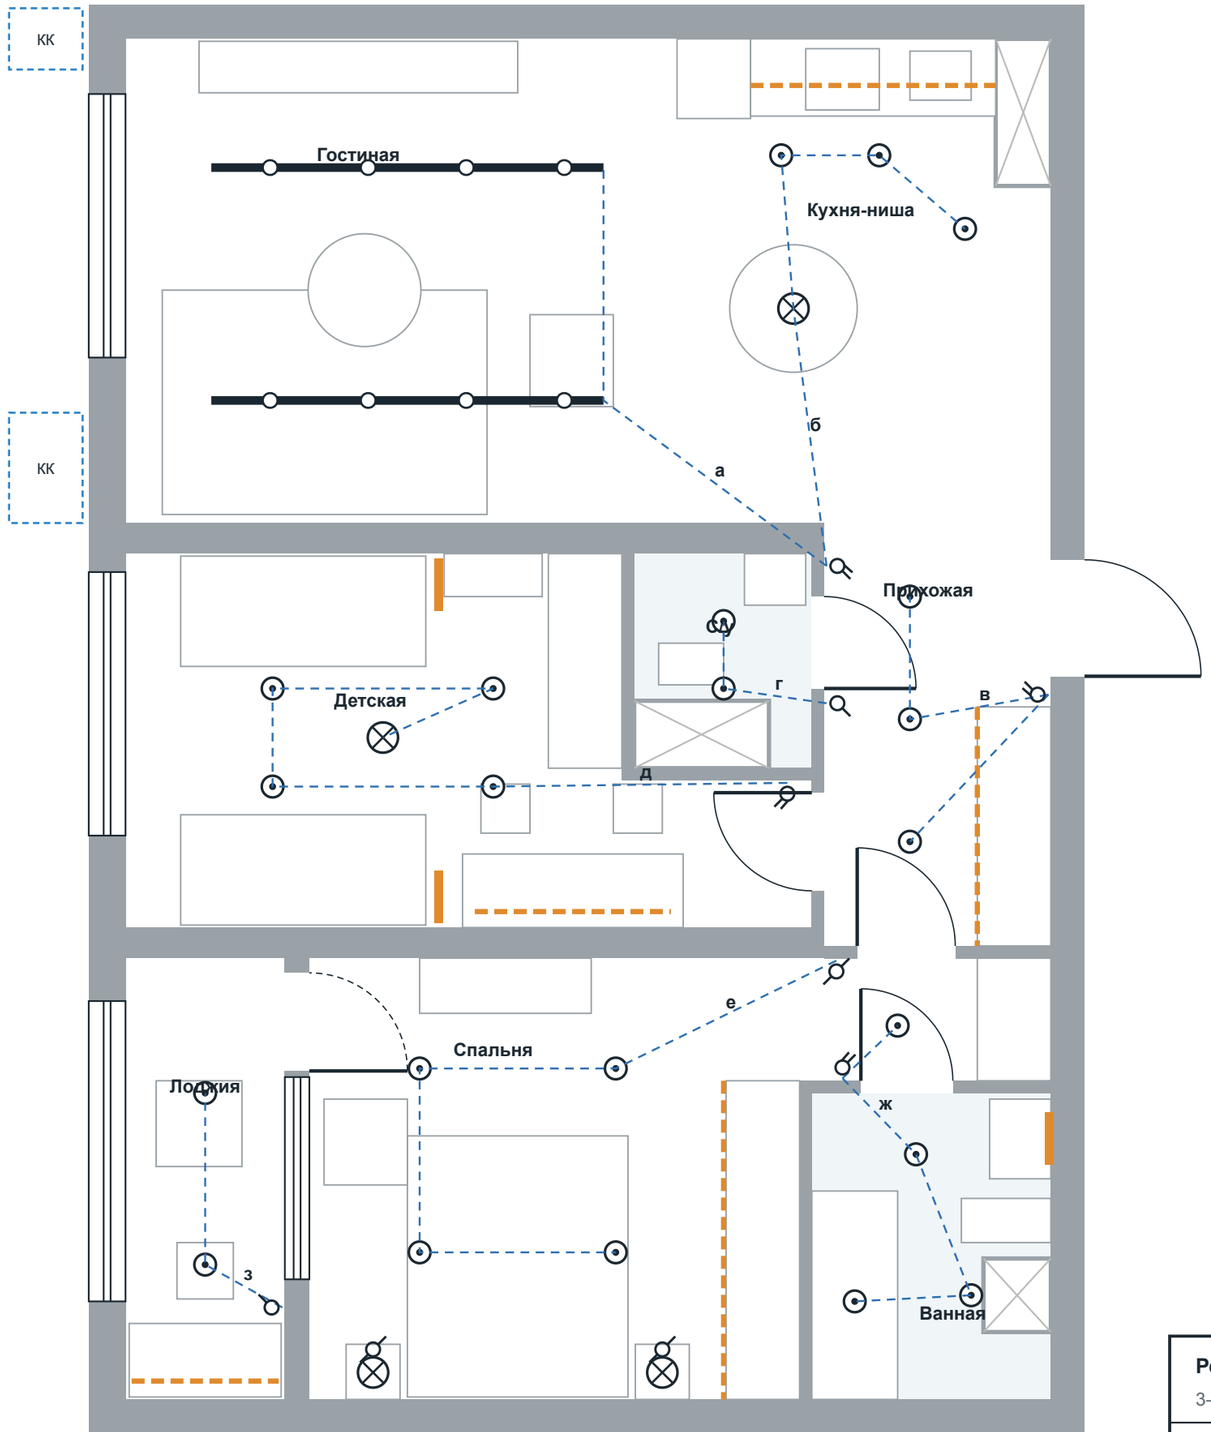

Освещение

▬	Магнитный трек с поворотными спотами	2 × 3,2 м
⊙	Точечный встраиваемый светильник	22 шт.
⊗	Подвесной светильник / бра	4 шт.
┅	LED-лента в профиле	~11 м
▮	Бра, ночник, подсветка зеркала	3 шт.
┄	Связь выключатель → группа света (а–з)	

Потолки

— Сухие зоны: натяжной матовый теневой (без плинтуса) или ГКЛ под покраску, отметка +3,00 / −50 мм под встраиваемые споты.

— Мокрые зоны: натяжной влагостойкий или ГКЛВ, споты IP44. Над ванной — ревизионный доступ к стоякам не закрывать.

— Кухня: короб под LED-ленту под верхними шкафами, отдельный выключатель.

— Сценарии: общий свет, акцент (трек), вечерний (бра, подсветка). Группы выводим на 2-клавишные выключатели у входов.

Ремонт квартиры · ЖК GreenLine Garden-2, блок 2, подъезд 2

3-комн., общая площадь 73,92 м² · концепция «Дала»


Потолки, свет, выключатели

Размеры в мм, отметки в м от чистого пола. Высота потолка 3,00 (уточнить)

Стадия: **Эскиз РП**

Дата	Основа	Масштаб	Лист	Листов
13.11.2026	планировка BI Group	1:50	05	10

06 · Розетки и выводы по группам

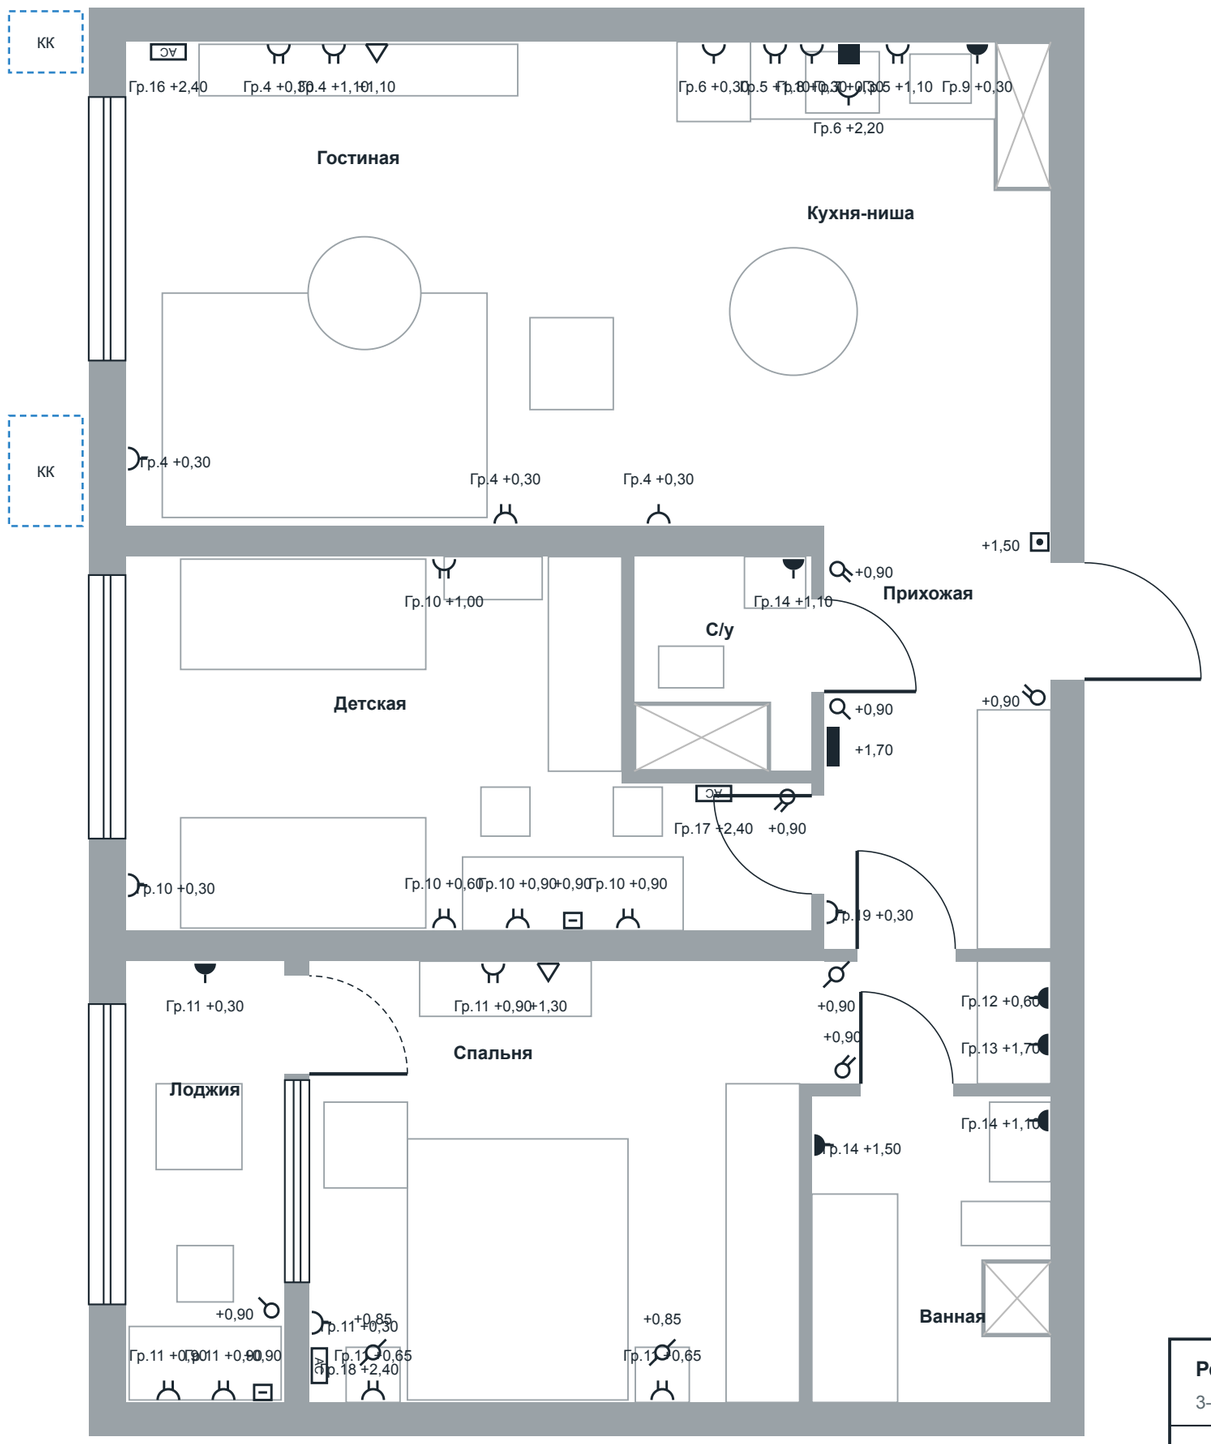

Электроустановочные изделия

	Розетка 1-мест., 16А	8 шт.
	Розетка 2-мест., 16А	14 шт.
	Розетка влагозащ. IP44	7 шт.
	Силовая: варочная 32А / духовка 16А	1 шт.
AC	Розетка кондиционера, 16А	3 шт.
	ТВ + интернет (RJ45)	2 шт.
	Интернет (RJ45)	2 шт.
	Выключатель 1-кл.	2 шт.
	Выключатель 2-кл.	4 шт.
	Выключатель проходной	3 шт.
	Домофон	1 шт.
	Щиток квартирный (уточнить)	1 шт.

Примечания

— Подпись у каждой точки: номер группы щита и высота оси от чистого пола. Группы и кабели — лист 08, трассы — лист 07.

— Блоки розеток в общей рамке, шаг 71 мм. За ТВ и на кухонном фартуке — по размерам мебели, после заказа кухни сверить.

— Детская: все розетки со шторками. Ванная и С/у: IP44, не ближе 600 мм от края ванны и раковины.

— Лоджия: розетки рабочего места +0,90 над столешницей, отдельная розетка под конвектор.

— Спальня: вывод ТВ на стене напротив кровати оставлен в резерве под заглушкой.

Ремонт квартиры · ЖК GreenLine Garden-2, блок 2, подъезд 2

3-комн., общая площадь 73,92 м² · концепция «Дала»


Розетки и выводы по группам

Размеры в мм, отметки в м от чистого пола. Высота потолка 3,00 (уточнить)

Стадия: **Эскиз РП**

Дата	Основа	Масштаб	Лист	Листов
13.11.2026	планировка BI Group	1:50	06	10

07 · Трассы кабельных линий

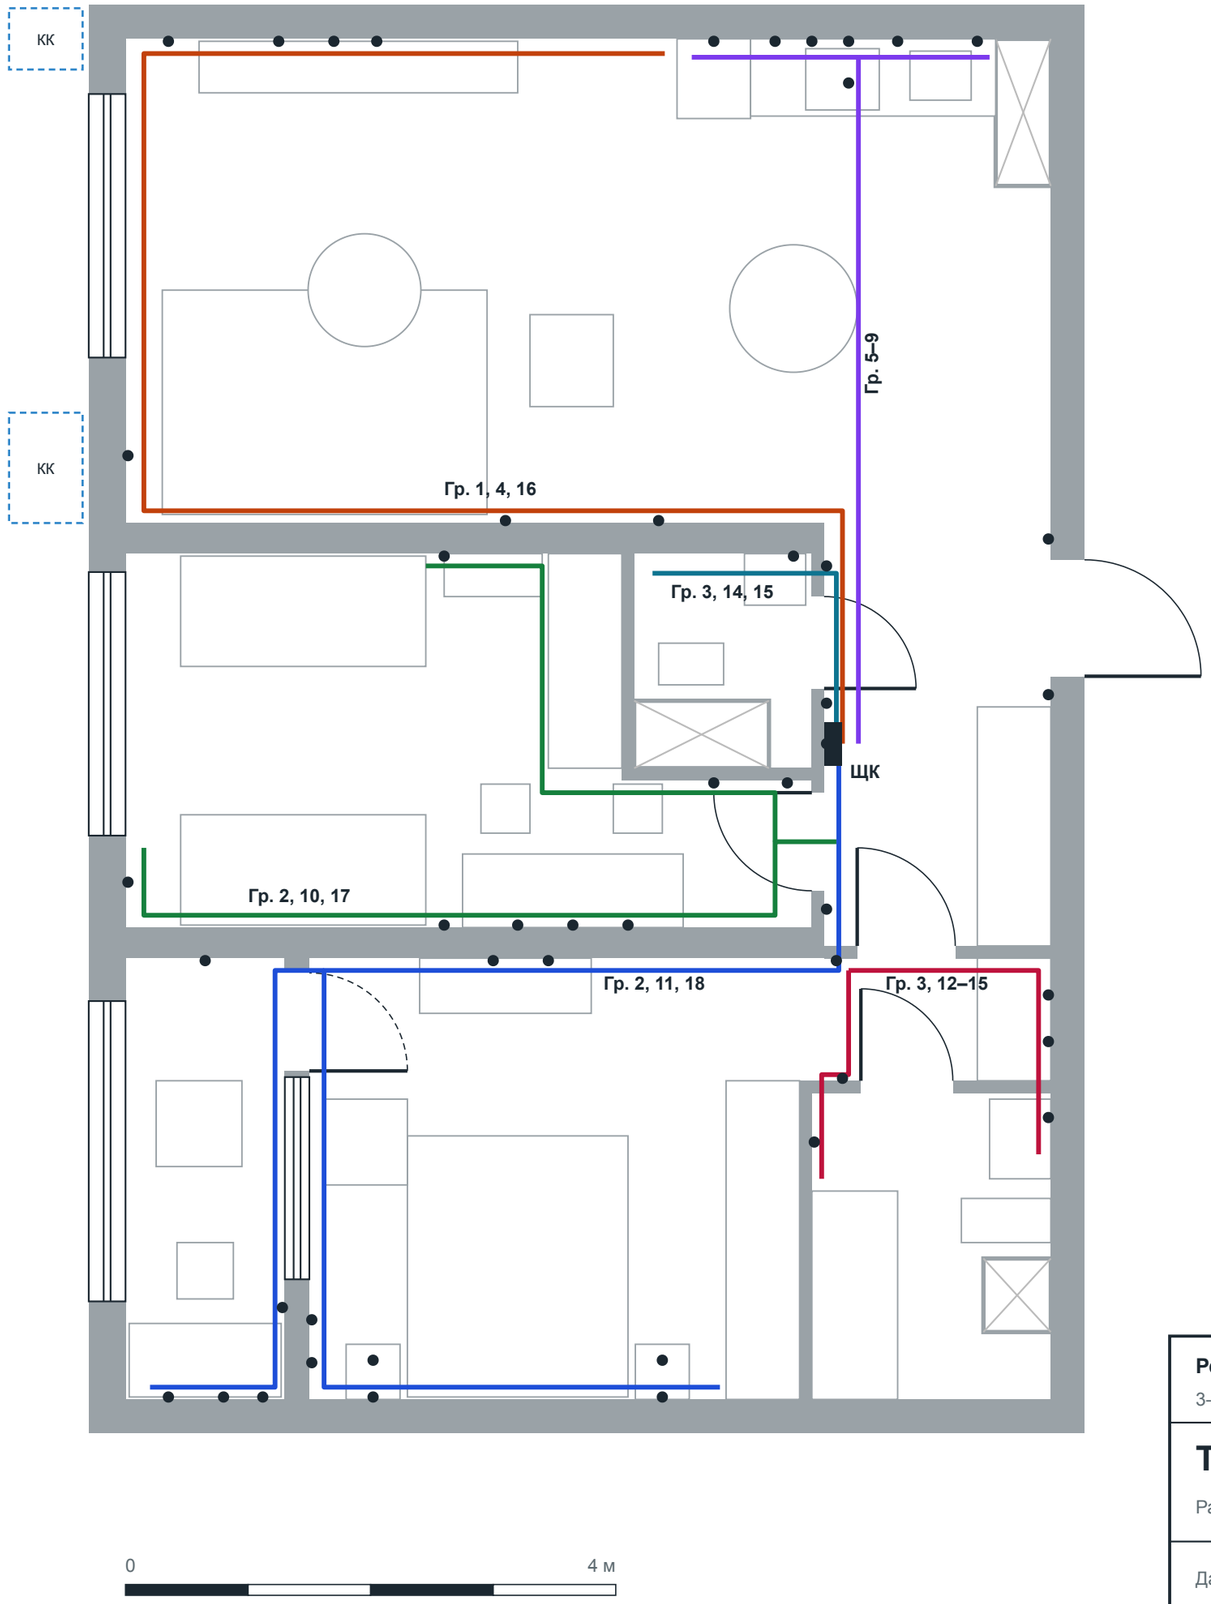

Кабельные трассы

—	Трасса: Гр. 1, 4, 16	
—	Трасса: Гр. 5–9	
—	Трасса: Гр. 3, 14, 15	
—	Трасса: Гр. 2, 10, 17	
—	Трасса: Гр. 2, 11, 18	
—	Трасса: Гр. 3, 12–15	
●	Точка подключения (опуск в штробе)	48 шт.

Способ прокладки

— Магистрали — по потолку в гофре ПВХ Ø20 за натяжным потолком, на клипсах, шаг 400 мм. Силовые и слаботочные раздельно, не ближе 100 мм.

— К розеткам и выключателям — вертикальные опуски в штробах 20×20 мм строго над точкой. Горизонтальные штробы только в газоблоке.

— В монолите (красные участки, лист 01) не штробить: обходить по газоблоку или в слое штукатурки.

— Пол не штробить: у застройщика «плавающий пол» с шумоизоляцией, штроба её разрушит.

— Распаечные коробки не используем: каждая группа идёт цельным кабелем от щита, ответвления — в подрозетниках на клеммах.

— Перед штукатуркой — фото всех трасс с рулеткой и исполнительная схема.

— Длины в журнале (лист 08) ориентировочные, с запасом 10%. Точно — после обмера.

Ремонт квартиры · ЖК GreenLine Garden-2, блок 2, подъезд 2

3-комн., общая площадь 73,92 м² · концепция «Дала»


Трассы кабельных линий

Размеры в мм, отметки в м от чистого пола. Высота потолка 3,00 (уточнить)

Стадия: **Эскиз РП**

Дата	Основа	Масштаб	Лист	Листов
13.11.2026	планировка BI Group	1:50	07	10

Однолинейная схема квартирного щита ЩК (36 модулей)

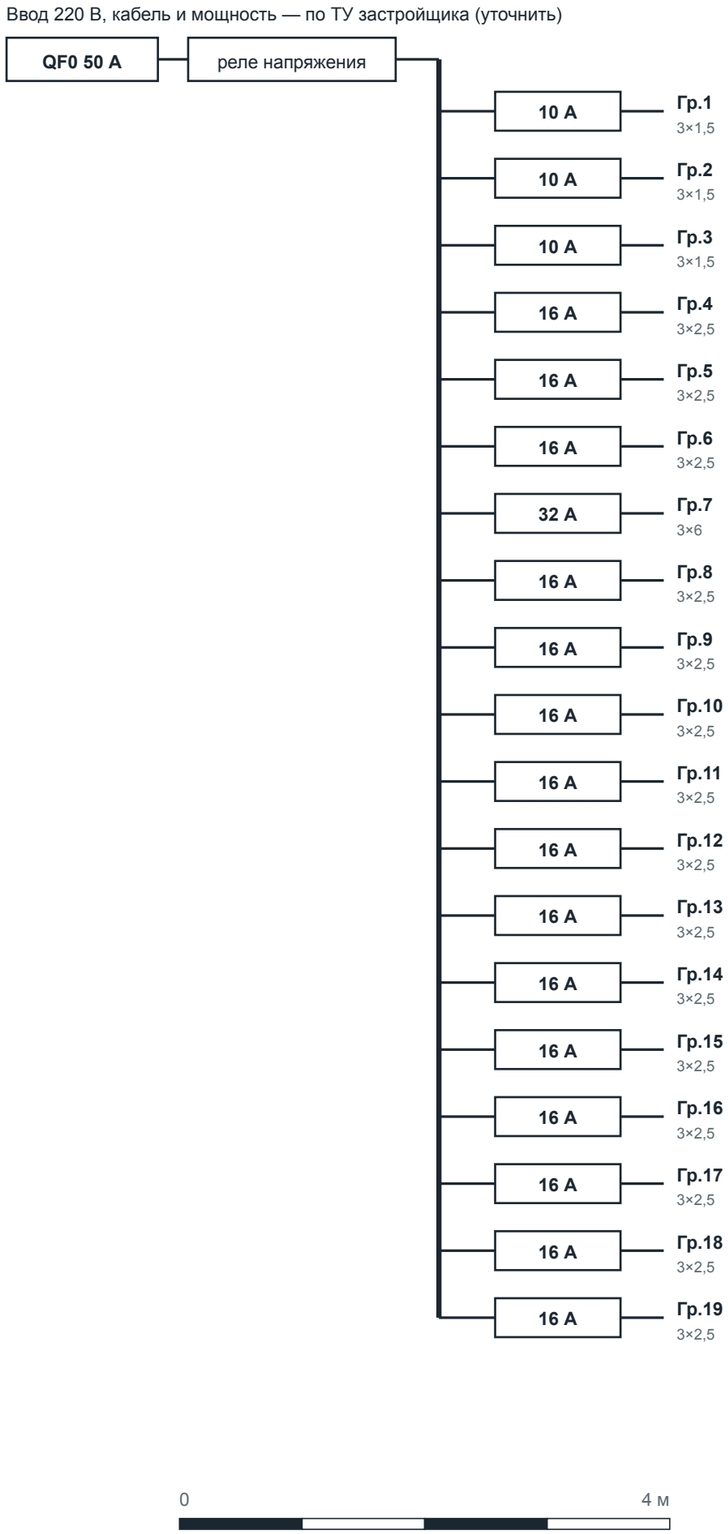

Кабельный журнал

Гр.	Назначение	Кабель	Автомат	Защита	Длина, м
1	Освещение: гостиная, кухня, прихожая	ВВГнг-LS 3×1,5	10 А, C	УЗО 40 А / 30 мА (свет)	38
2	Освещение: детская, спальня, лоджия	ВВГнг-LS 3×1,5	10 А, C	то же	42
3	Освещение и вентиляторы: С/у, ванная	ВВГнг-LS 3×1,5	10 А, C	то же	22
4	Розетки: гостиная	ВВГнг-LS 3×2,5	16 А, C	УЗО 40 А / 30 мА (розетки)	34
5	Розетки: кухонный фартук	ВВГнг-LS 3×2,5	16 А, C	дифавтомат 30 мА	16
6	Холодильник, вытяжка	ВВГнг-LS 3×2,5	16 А, C	дифавтомат 30 мА	15
7	Варочная панель (индукция)	ВВГнг-LS 3×6	32 А, C	дифавтомат 30 мА	14
8	Духовой шкаф	ВВГнг-LS 3×2,5	16 А, C	дифавтомат 30 мА	14
9	Посудомоечная машина	ВВГнг-LS 3×2,5	16 А, C	дифавтомат 30 мА	16
10	Розетки: детская	ВВГнг-LS 3×2,5	16 А, C	УЗО 40 А / 30 мА (розетки)	30
11	Розетки: спальня, рабочее место на лоджии	ВВГнг-LS 3×2,5	16 А, C	то же	44
12	Стиральная машина	ВВГнг-LS 3×2,5	16 А, C	дифавтомат 30 мА	9
13	Сушильная машина	ВВГнг-LS 3×2,5	16 А, C	дифавтомат 30 мА	9
14	Розетки: ванная, С/у, полотенцесушитель	ВВГнг-LS 3×2,5	16 А, C	дифавтомат 10 мА	18
15	Тёплый пол: С/у, ванная, лоджия	ВВГнг-LS 3×2,5	16 А, C	дифавтомат 30 мА	24
16	Кондиционер: гостиная	ВВГнг-LS 3×2,5	16 А, C	дифавтомат 30 мА	20
17	Кондиционер: детская	ВВГнг-LS 3×2,5	16 А, C	дифавтомат 30 мА	8
18	Кондиционер: спальня	ВВГнг-LS 3×2,5	16 А, C	дифавтомат 30 мА	16
19	Розетки: прихожая, роутер, слаботочный щит	ВВГнг-LS 3×2,5	16 А, C	УЗО 40 А / 30 мА (розетки)	8

Итого кабель: 3×1,5 — 102 м · 3×2,5 — 281 м · 3×6 — 14 м

— Два УЗО на группы без дифавтоматов: свет и розетки комнат. Мокрые зоны и техника — индивидуальные дифавтоматы.

— Слаботочный щит рядом с ЩК: роутер, свитч, витая пара Cat.6 в гостиную, детскую, спальню и на лоджию.

— Номиналы и сечения — проектное решение; окончательно подтверждает электрик с допуском после получения ТУ на мощность.

Ремонт квартиры · ЖК GreenLine Garden-2, блок 2, подъезд 2


3-комн., общая площадь 73,92 м² · концепция «Дала»

Схема щита и кабельный журнал

Размеры в мм, отметки в м от чистого пола. Высота потолка 3,00 (уточнить)

Стадия: **Эскиз РП**

Дата	Основа	Масштаб	Лист	Листов
13.11.2026	планировка BI Group	1:50	08	10

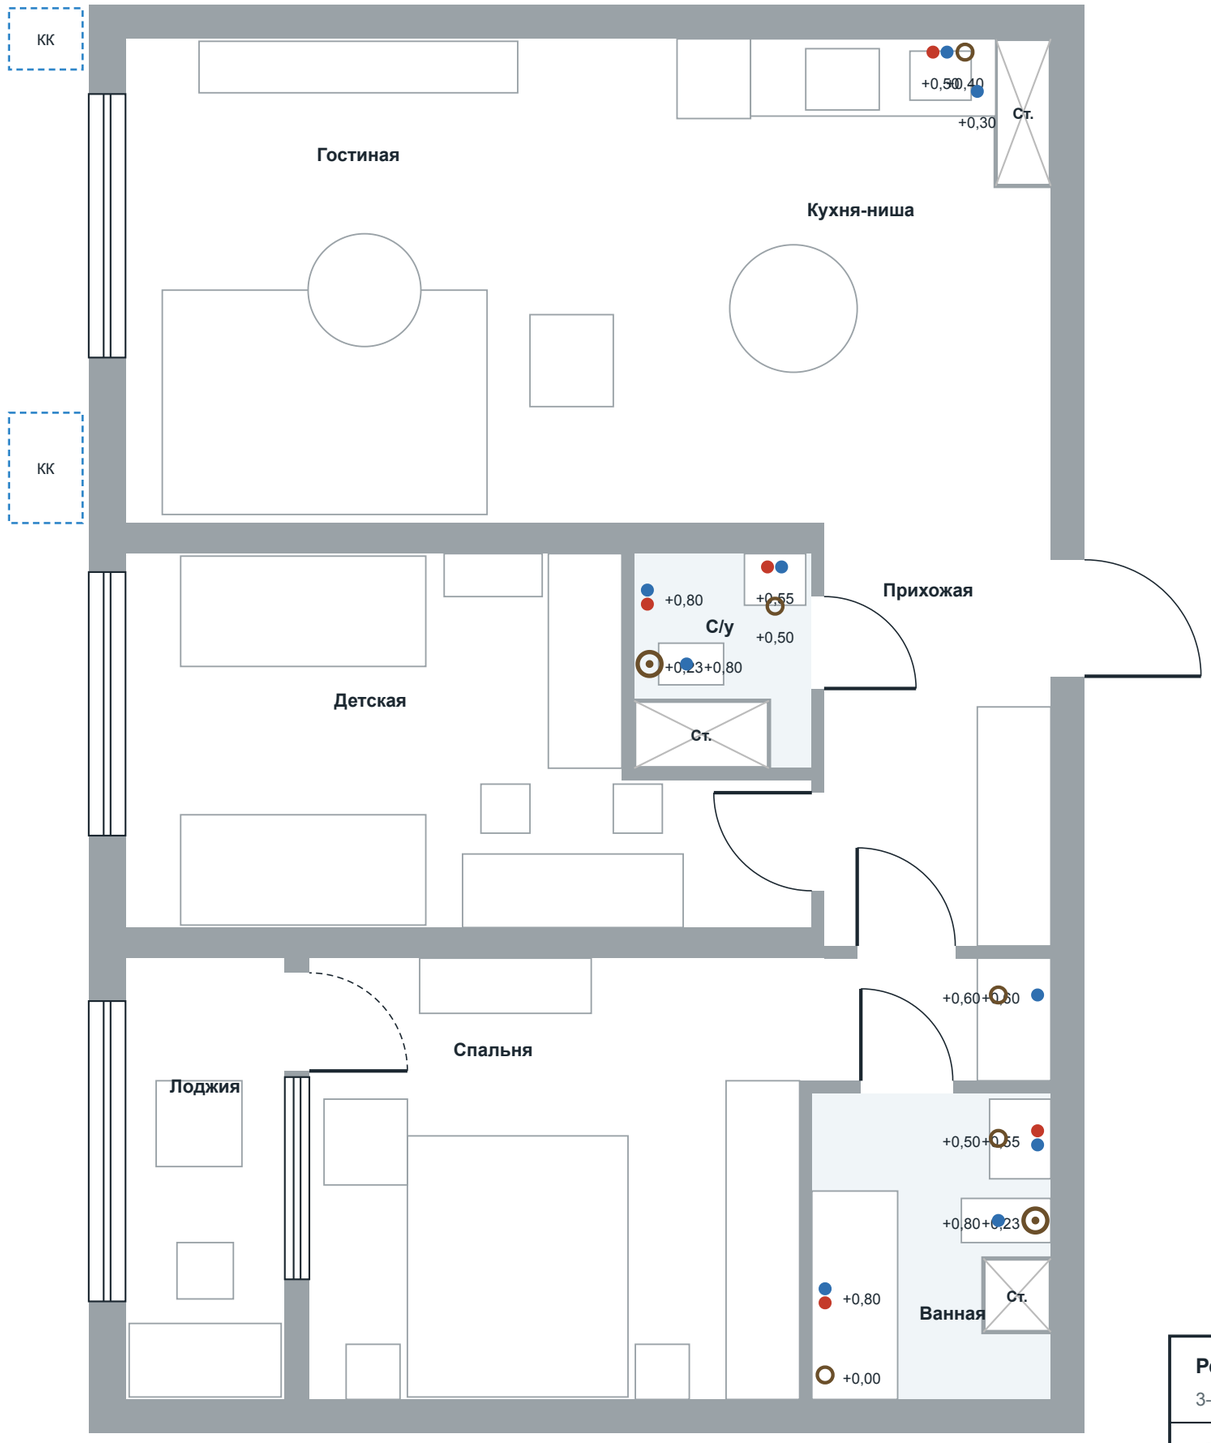

Сантехнические выводы

●●	Выводы ХВС + ГВС	5 шт.
●	Вывод ХВС	4 шт.
○	Канализация Ø50	5 шт.
◎	Канализация Ø110	2 шт.

Точки подключения

Мойка: ХВС/ГВС	+0,50
Мойка + ПММ: К50	+0,40
ПММ: ХВС ¾"	+0,30
С/у, унитаз (инсталляция): К110	+0,23
С/у, инсталляция: ХВС	+0,80
С/у, гигиенич. душ: ХВС/ГВС	+0,80
С/у, раковина: ХВС/ГВС	+0,55
С/у, раковина: К50	+0,50
Ванна, смеситель: ХВС/ГВС	+0,80
Ванна: К50 (слив)	+0,00
Ванная, унитаз (инсталляция): К110	+0,23
Ванная, инсталляция: ХВС	+0,80
Ванная, раковина: ХВС/ГВС	+0,55
Ванная, раковина: К50	+0,50
Постирочная: ХВС ¾"	+0,60
Постирочная: К50 (через стену в ванную)	+0,60

— Разводка от стояков в коробах, коллекторная, полипропилен или сшитый полиэтилен; краны и фильтры — в ревизионном люке.

— Уклон канализации 2–3%. Слив ванны идёт к стояку вдоль наружной стены около 1,5 м: проверить высоту, при необходимости подиум 50 мм.

— Постирочная стоит за стеной ванной: подача и слив проходят сквозь новую перегородку, гильзы закладываются при кладке.

— Полотенцесушитель электрический (лист 06), стояк ГВС не трогаем.

Ремонт квартиры · ЖК GreenLine Garden-2, блок 2, подъезд 2

3-комн., общая площадь 73,92 м² · концепция «Дала»


Сантехника

Размеры в мм, отметки в м от чистого пола. Высота потолка 3,00 (уточнить)

Стадия: **Эскиз РП**

Дата	Основа	Масштаб	Лист	Листов
13.11.2026	планировка BI Group	1:50	09	10

10 · Обмерный лист

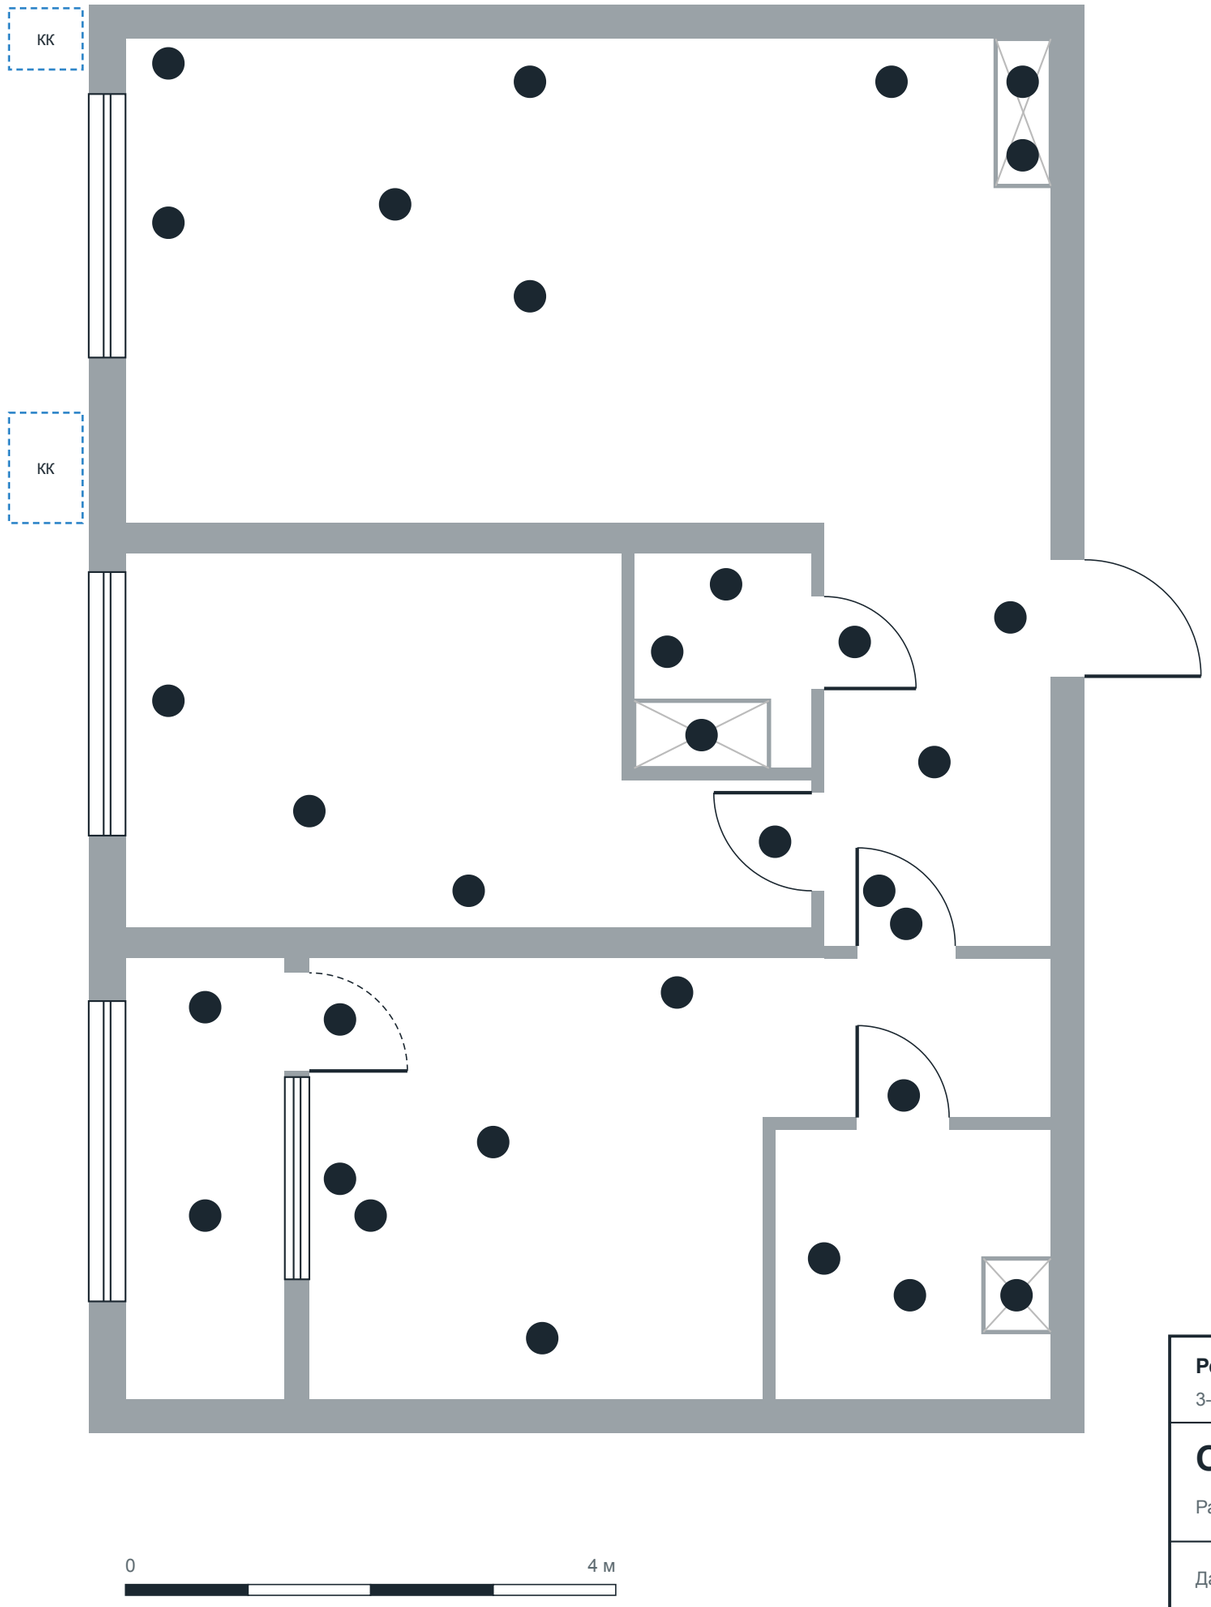

Заполнить на объекте, мм

1	Гостиная: Стена ТВ: от фасада до правой стены проект 7550	_____
2	Гостиная: Глубина: от стены ТВ до стены детской проект 3950	_____
3	Гостиная: Диагональ (проверка углов) проект 8521	_____
4	Гостиная: От угла до окна проект 450	_____
5	Гостиная: Ширина оконного проёма проект 2150	_____
6	Кухня: Стена: от фасада до короба проект 7100	_____
7	Кухня: Короб: ширина проект 450	_____
8	Кухня: Короб: глубина проект 1200	_____
9	Прихожая: Ширина проект 1850	_____
10	Прихожая: Длина: от гостиной до двери спальни проект 3450	_____
11	Прихожая: Входной проём проект 950	_____
12	Детская: Длина вдоль стены спальни проект 5600	_____
13	Детская: Глубина у окна проект 3050	_____
14	Детская: Ширина оконного проёма проект 2150	_____
15	Детская: Дверной проём проект 800	_____
16	С/у: Ширина проект 1450	_____
17	С/у: Глубина проект 1750	_____
18	С/у: Короб: длина по стене проект 1100	_____
19	С/у: Дверной проём проект 750	_____
20	Спальня: Ширина у входа: от лоджии до правой стены проект 6050	_____
21	Спальня: Длина: от детской до наружной стены проект 3600	_____
22	Спальня: От лоджии до ванной проект 3700	_____
23	Спальня: Диагональ (проверка углов) проект 5162	_____
24	Спальня: Дверной проём проект 800	_____
25	Лоджия: Ширина проект 1300	_____
26	Лоджия: Длина проект 3600	_____
27	Лоджия: Балконная дверь проект 800	_____
28	Лоджия: Окно из спальни проект 1650	_____
29	Ванная: Ширина проект 2250	_____
30	Ванная: Глубина проект 2200	_____
31	Ванная: Короб: длина по стене проект 600	_____
32	Ванная: Дверной проём проект 750	_____
33	Потолок: гостиная проект 3000	_____
34	Потолок: детская проект 3000	_____
35	Потолок: спальня проект 3000	_____
36	Потолок: прихожая проект 3000	_____
37	Потолок: С/у проект 3000	_____
38	Потолок: ванная проект 3000	_____
39	Низ окна от пола проект 250	_____
40	Высота оконного проёма проект 2500	_____
41	Высота дверных проёмов проект 2100	_____

Ремонт квартиры · ЖК GreenLine Garden-2, блок 2, подъезд 2

3-комн., общая площадь 73,92 м² · концепция «Дала»

Обмерный лист

Размеры в мм, отметки в м от чистого пола. Высота потолка 3,00 (уточнить)

Стадия: **Эскиз РП**

Дата	Основа	Масштаб	Лист	Листов
13.11.2026	планировка BI Group	1:50	10	10